

1 planta de situação
1 : 1000

Quadro de Áreas - 1° Pavimento				
Número	Nome	Área(m²)	Pé direito(m)	Nível
1	Quarto 4	33,70 m²	2,60	Planta baixa 1° Pav
2	Quarto 3	30,73 m²	2,60	Planta baixa 1° Pav
3	Closet 3	2,76 m²	2,60	Planta baixa 1° Pav
4	Quarto 2	26,59 m²	2,60	Planta baixa 1° Pav
5	Banheiro 2	7,06 m²	2,60	Planta baixa 1° Pav
6	Closet	1,98 m²	2,60	Planta baixa 1° Pav
7	Área Comum	23,10 m²	2,60	Planta baixa 1° Pav
8	Banheiro 4	6,86 m²	2,60	Planta baixa 1° Pav
9	Baneiro 3	6,61 m²	2,60	Planta baixa 1° Pav
10	Varanda Coberta	10,98 m²	2,60	Planta baixa 1° Pav
11	Closet 4	2,90 m²	2,60	Planta baixa 1° Pav
Área Util Pavimento		153,27 m²		

Quadro de Áreas Térreo				
Número	Nome	Área	Pé direito	Nível
46	Lavabo	2,90 m²		Planta Baixa Térreo LY
66	Quarto 1	22,05 m²	3,00	Planta Baixa Térreo LY
67	Banheiro 1	4,88 m²	3,00	Planta Baixa Térreo LY
68	Closet 1	2,97 m²	3,00	Planta Baixa Térreo LY
73	Área Gourmet	7,98 m²	3,00	Planta Baixa Térreo LY
74	Cozinha	14,55 m²	3,00	Planta Baixa Térreo LY
75	Sala de estar	30,81 m²	3,00	Planta Baixa Térreo LY
76	Sala de Jantar	31,51 m²	3,00	Planta Baixa Térreo LY
79	Despesa	2,49 m²	3,00	Planta Baixa Térreo LY
84	Quarto de Serviço	9,39 m²	3,00	Planta Baixa Térreo LY
85	Área de Serviço	4,70 m²	3,00	Planta Baixa Térreo LY
87	Banheiro de Serviço	5,11 m²	3,00	Planta Baixa Térreo LY
Área Util Pavimento		139,34 m²		

QUADRO DE ÁREAS

ÁREA DO TERRENO	856,93 m²
ÁREA CONSTRUÍDA - SUBSOLO	49,73 m²
ÁREA CONSTRUÍDA - TÉRREO	158,46 m²
ÁREA CONSTRUÍDA - 1º PAVIMENTO	164,83m²
ÁREA PERMEÁVEL	530,76m²
TAXA DE OCUPAÇÃO	38,06%
ÁREA TOTAL DE CONSTRUÇÃO(TÉRREO+1ºPAVTO)	323,29m²

Especificações	
ITEM	ESPECIFICAÇÃO
1	Calçada Cimentada
2	Rampa de aAcesso - Bloco intertravado
3	Telha Montecarmelo, tipo Romam Acabamento Esmaltado
4	Grama Tipo Batatais


Quadro Geral de Portas				
CÓDIGO	Altura	Largura	QNT.	Descrição
P1	2,13	0,81	12	Porta Pivotante de Madeira
P2	2,15	0,90	6	Porta Deslizante
P3	2,21	2,82	2	Porta Deslizante de Vidro

Quadro Geral de Janelas					
CÓDIGO	Altura	Altura do peitoril	Largura	QNT.	Descrição
J1	1,22	1,00	2,48	3	Janela Dupla Fixa
J2	0,60	1,20	1,20	4	Janela de Correr
J3	0,60	1,50	0,80	5	Janela Pivotante
J4	2,12	0,70	4,98	1	Janela Quádrupla Fixa
J5	0,91	0,80	1,91	2	Janela em L
J6	1,22	0,80	4,98	1	Janela Quádrupla

COMPARTIMENTO \ MATERIAIS	SUPERFÍCIES: (1) PISO CERÂMICO ESMALTADO - 20X20	(2) PISO EM PORCELANATO POLIDO - 30X30	(3) PISO LAMINADO DE MADEIRA	(1) PINTURA ACRÍLICA BRANCA	FORRO EM GESSO PINTADO	CONCRETO APARENTE	OBSERVAÇÕES
Sala de Estar	●	●	●	●	●		
Sala de Jantar		●		●	●		
Quarto 1			●	●	●		
Closet 1			●	●	●		
Banheiro 1	●			●	●		
Lavabo	●			●	●		
Área Gourmet		●		●	●		
Despensa		●		●	●		
Cozinha	●			●	●		
Área de Serviço	●			●	●		
Quarto de Serviço			●	●	●		
Banheiro de serviço	●			●	●		
Varanda Coberta		●		●	●		
Área Comum		●		●	●		
Quarto 2			●	●	●		
Banheiro 2	●			●	●		
Closet 2			●	●	●		
Quarto 3			●	●	●		
Banheiro 3	●			●	●		
Closet 3			●	●	●		
Quarto 4			●	●	●		
Banheiro 4	●			●	●		
Closet 4			●	●	●		
Garagem	●			●		●	


LEGENDAS

○ PISOS E SUPERFÍCIES HORIZONTAIS
△ VEDAÇÕES E SUPERFÍCIES VERTICAIS
□ TETOS

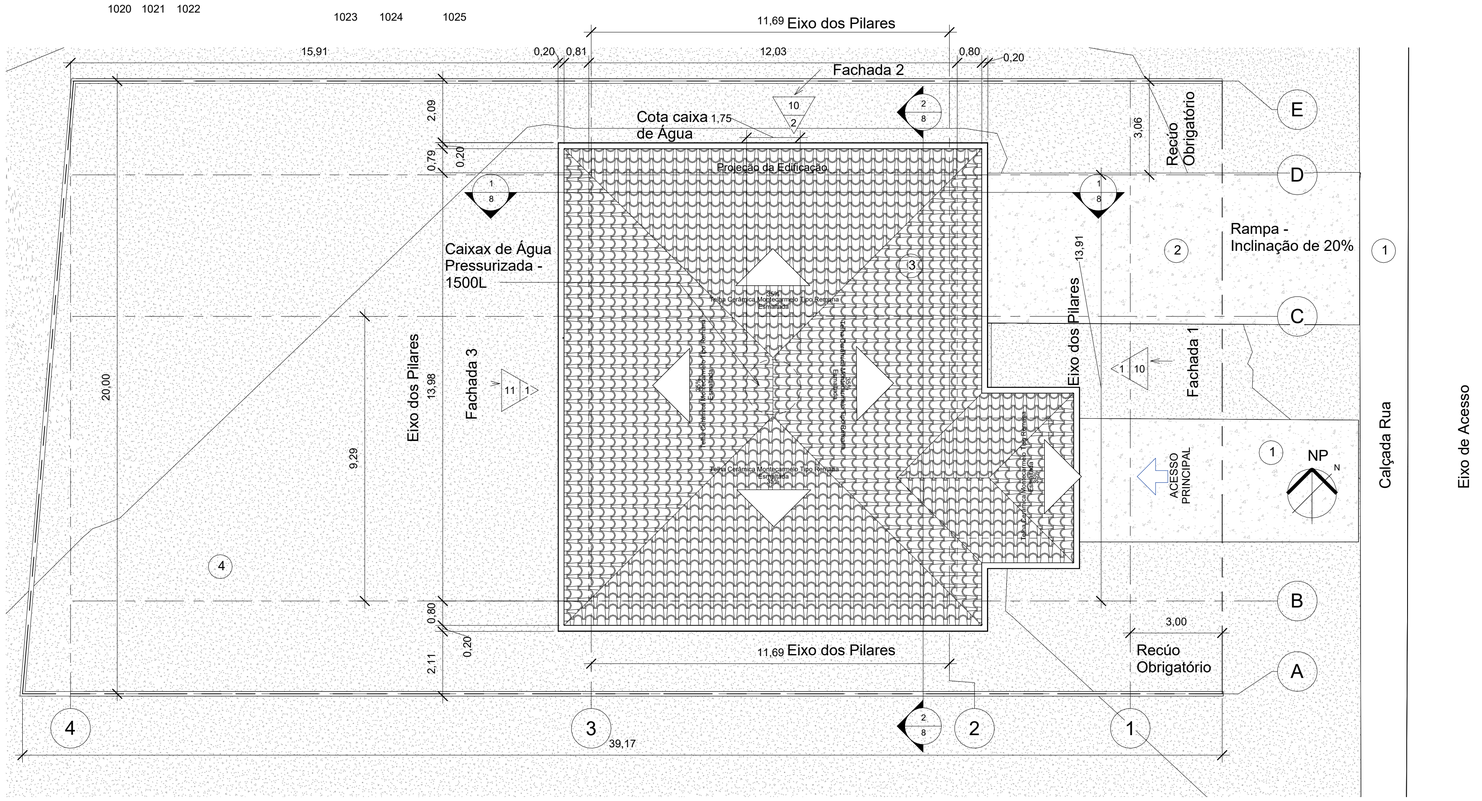

2 Planta de Locação
1 : 100

SHIS QL 23 Conjunto 3 Lote 5		
PE	Projeto Executivo Planta de Sit. e Loc.	1
ALUNO: Gabriel Guimarães Horta	MAT: 222005288	ESC: Como indicado

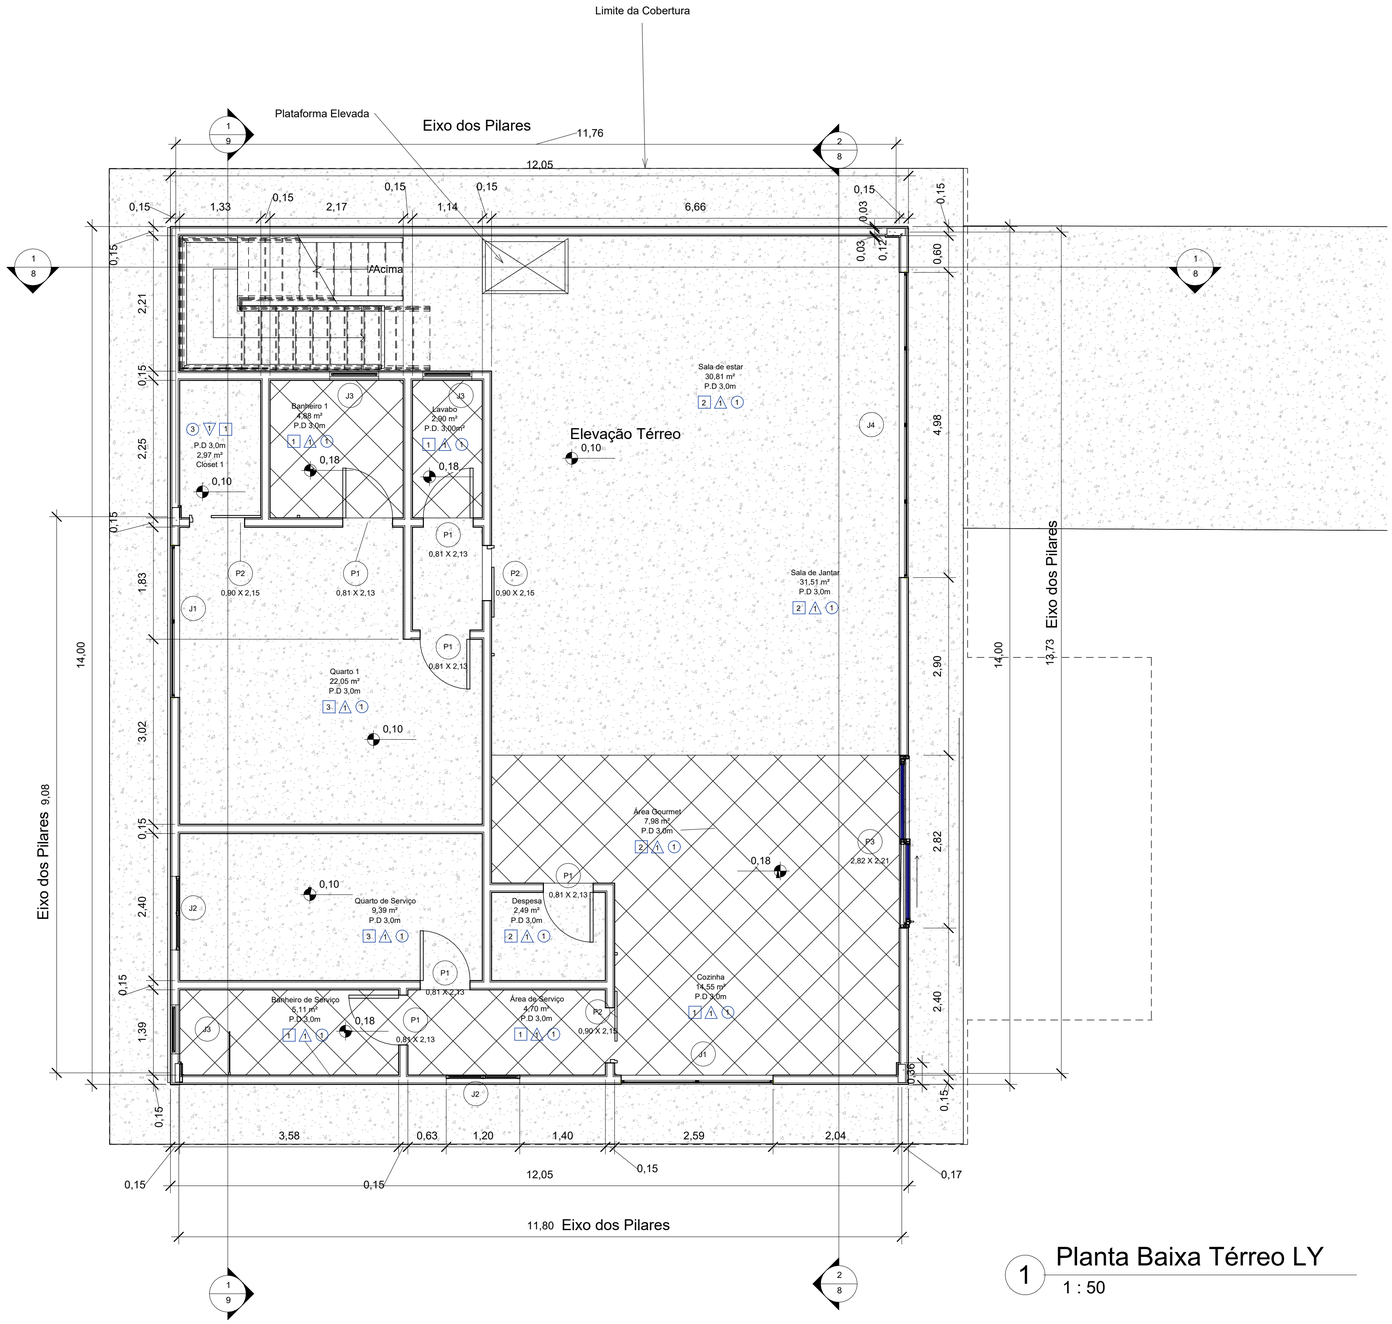

1 Planta Baixa Térreo LY
1 : 50

COMPARTIMENTO \ MATERIAIS	SUPERFÍCIES: 1 PISO CERÂMICO ESMALTADO - 20X20	2 PISO EM PORCELANATO POLIDO - 30X30	3 PISO LAMINADO DE MADEIRA	○	1 PINTURA ACRILICA BRANCA	△	△	△	1 FORRO EM GESSO PINTADO	2 CONCRETO APARENTE	□	□	OBSERVAÇÕES
Sala de Estar	●	●	●		●				●				
Sala de Jantar		●			●				●				
Quarto 1			●		●				●				
Closet 1			●		●				●				
Banheiro 1	●				●				●				
Lavabo	●				●				●				
Área Gourmet		●			●				●				
Despensa		●			●				●				
Cozinha	●				●				●				
Área de Serviço	●				●				●				
Quarto de Serviço			●		●				●				
Banheiro de serviço	●				●				●				
Varanda Coberta		●			●				●				
Área Comum		●			●				●				
Quarto 2			●		●				●				
Banheiro 2	●				●				●				
Closet 2			●		●				●				
Quarto 3			●		●				●				
Banheiro 3	●				●				●				
Closet 3			●		●				●				
Quarto 4			●		●				●				
Banheiro 4	●				●				●				
Closet 4			●		●				●				
Garagem	●				●					●			

LEGENDAS

○ PISOS E SUPERFÍCIES HORIZONTAIS
△ VEDAÇÕES E SUPERFÍCIES VERTICAIS
□ TETOS


Quadro de Áreas Térreo

Número	Nome	Área	Pé direito	Nível
46	Lavabo	2,90 m²		Planta Baixa Térreo LY
66	Quarto 1	22,05 m²	3,00	Planta Baixa Térreo LY
67	Banheiro 1	4,88 m²	3,00	Planta Baixa Térreo LY
68	Closet 1	2,97 m²	3,00	Planta Baixa Térreo LY
73	Área Gourmet	7,98 m²	3,00	Planta Baixa Térreo LY
74	Cozinha	14,55 m²	3,00	Planta Baixa Térreo LY
75	Sala de estar	30,81 m²	3,00	Planta Baixa Térreo LY
76	Sala de Jantar	31,51 m²	3,00	Planta Baixa Térreo LY
79	Despesa	2,49 m²	3,00	Planta Baixa Térreo LY
84	Quarto de Serviço	9,39 m²	3,00	Planta Baixa Térreo LY
85	Área de Serviço	4,70 m²	3,00	Planta Baixa Térreo LY
87	Banheiro de Serviço	5,11 m²	3,00	Planta Baixa Térreo LY
Área Util Pavimento		139,34 m²		

SHIS QL 23 Conjunto 3 Lote 5

PE | Projeto Executivo | Planta Baixa Térreo | 2

ALUNO: Gabriel Guimarães Horta | MAT. 222005288 | ESC. 1 : 50

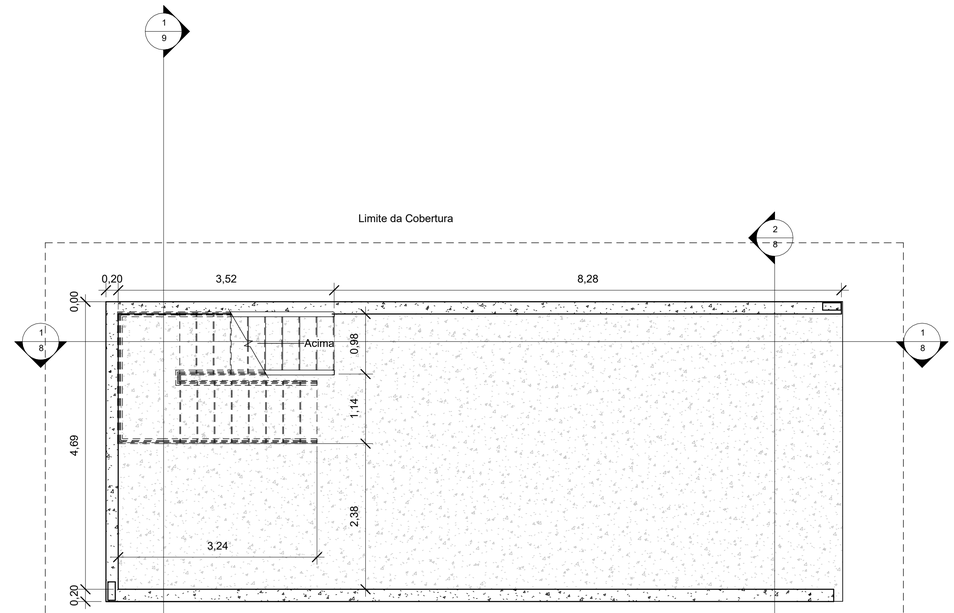

1 Planta Baixa - Subsolo

1 : 50

COMPARTIMENTO \ MATERIAIS	SUPERFÍCIES											OBSERVAÇÕES
	1 PISO CERÂMICO ESMALTADO - 20X20	2 PISO EM PORCELANATO POLIDO - 30X30	3 PISO LAMINADO DE MADEIRA	○	1 PINTURA ACRÍLICA BRANCA	△	△	△	1 FORRO EM GESSO PINTADO	2 CONCRETO APARENTE	□	□	
Sala de Estar	●	●	●		●				●				
Sala de Jantar		●			●				●				
Quarto 1			●		●				●				
Closet 1			●		●				●				
Banheiro 1	●				●				●				
Lavabo	●				●				●				
Área Gourmet		●			●				●				
Despensa		●			●				●				
Cozinha	●				●				●				
Área de Serviço	●				●				●				
Quarto de Serviço			●		●				●				
Banheiro de serviço	●				●				●				
Varanda Coberta		●			●				●				
Área Comum		●			●				●				
Quarto 2			●		●				●				
Banheiro 2	●				●				●				
Closet 2			●		●				●				
Quarto 3			●		●				●				
Banheiro 3	●				●				●				
Closet 3			●		●				●				
Quarto 4			●		●				●				
Banheiro 4	●				●				●				
Closet 4			●		●				●				
Garagem	●				●					●			


LEGENDAS

○ PISOS E SUPERFÍCIES HORIZONTAIS

△ VEDAÇÕES E SUPERFÍCIES VERTICAIS

□ TETOS

SHIS QL 23 Conjunto 3 Lote 5		
PE	Projeto Executivo Planta Baixa Subsolo	3
ALUNO: Projetista	MAT.: Autor	ESC.: 1 : 50

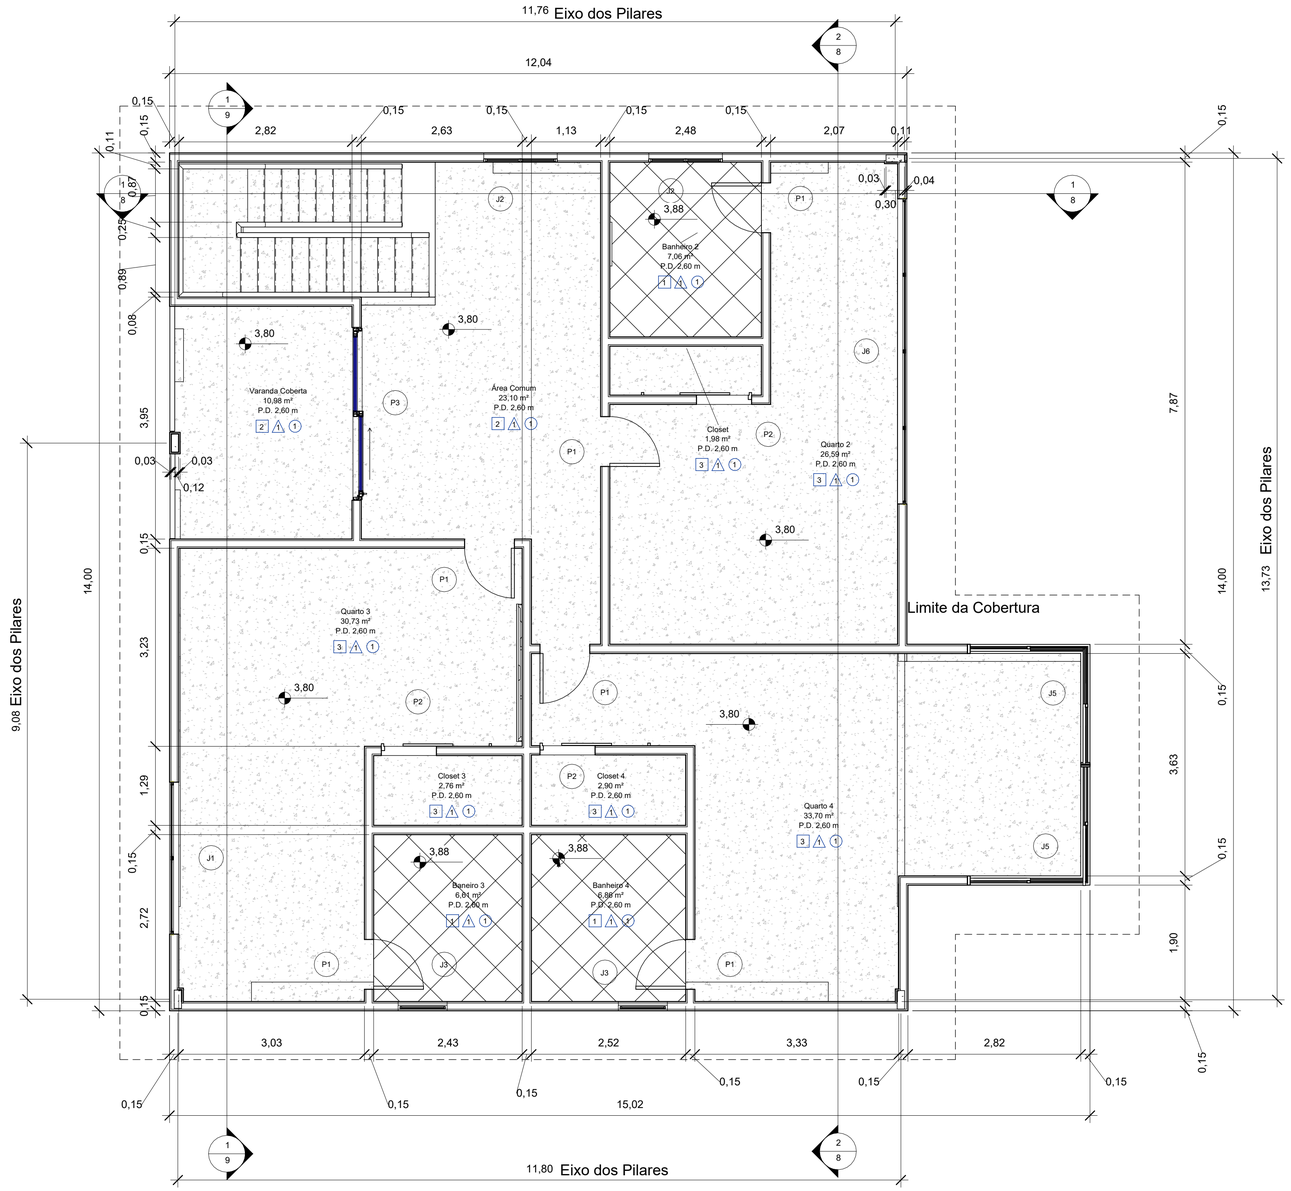

1 Planta baixa 1° Pav

1 : 50

COMPARTIMENTO / MATERIAIS	SUPERFÍCIES: PISO CERÂMICO ESMALTADO - 20X20 (1)	PISO EM PORCELANATO POLIDO - 20X20 (2)	PISO LAMINADO DE MADEIRA (3)	○	PINTURA ACRÍLICA BRANCA (1)	△	△	△	FORRO EM GESSO PINTADO (1)	CONCRETO APARENTE (2)	□	□	OBSERVAÇÕES
Sala de Estar	●	●	●		●				●				
Sala de Jantar		●			●				●				
Quarto 1			●		●				●				
Closet 1			●		●				●				
Banheiro 1	●				●				●				
Lavabo	●				●				●				
Área Gourmet		●			●				●				
Despensa		●			●				●				
Cozinha	●				●				●				
Área de Serviço	●				●				●				
Quarto de Serviço			●		●				●				
Banheiro de serviço	●				●				●				
Varanda Coberta		●			●				●				
Área Comum		●			●				●				
Quarto 2			●		●				●				
Banheiro 2	●				●				●				
Closet 2			●		●				●				
Quarto 3			●		●				●				
Banheiro 3	●				●				●				
Closet 3			●		●				●				
Quarto 4			●		●				●				
Banheiro 4	●				●				●				
Closet 4			●		●				●				
Garagem	●				●					●			

LEGENDAS

○ PISOS E SUPERFÍCIES HORIZONTAIS

△ VEDAÇÕES E SUPERFÍCIES VERTICAIS

□ TETOS

Quadro de Áreas - 1° Pavimento

Número	Nome	Área(m²)	Pé direito(m)	Nível
1	Quarto 4	33,70 m²	2,60	Planta baixa 1° Pav
2	Quarto 3	30,73 m²	2,60	Planta baixa 1° Pav
3	Closet 3	2,76 m²	2,60	Planta baixa 1° Pav
4	Quarto 2	26,59 m²	2,60	Planta baixa 1° Pav
5	Banheiro 2	7,06 m²	2,60	Planta baixa 1° Pav
6	Closet	1,98 m²	2,60	Planta baixa 1° Pav
7	Área Comum	23,10 m²	2,60	Planta baixa 1° Pav
8	Banheiro 4	6,86 m²	2,60	Planta baixa 1° Pav
9	Baneiro 3	6,61 m²	2,60	Planta baixa 1° Pav
10	Varanda Coberta	10,98 m²	2,60	Planta baixa 1° Pav
11	Closet 4	2,90 m²	2,60	Planta baixa 1° Pav
Área Util Pavimento		153,27 m²		

SHIS QL 23 Conjunto 3 Lote 5

PE

Projeto Executivo


Plantas Baixa 1° Pav

4

ALUNO: Gabriel Guimarães Horta

MAT. 222005288

ESC: 1 : 50

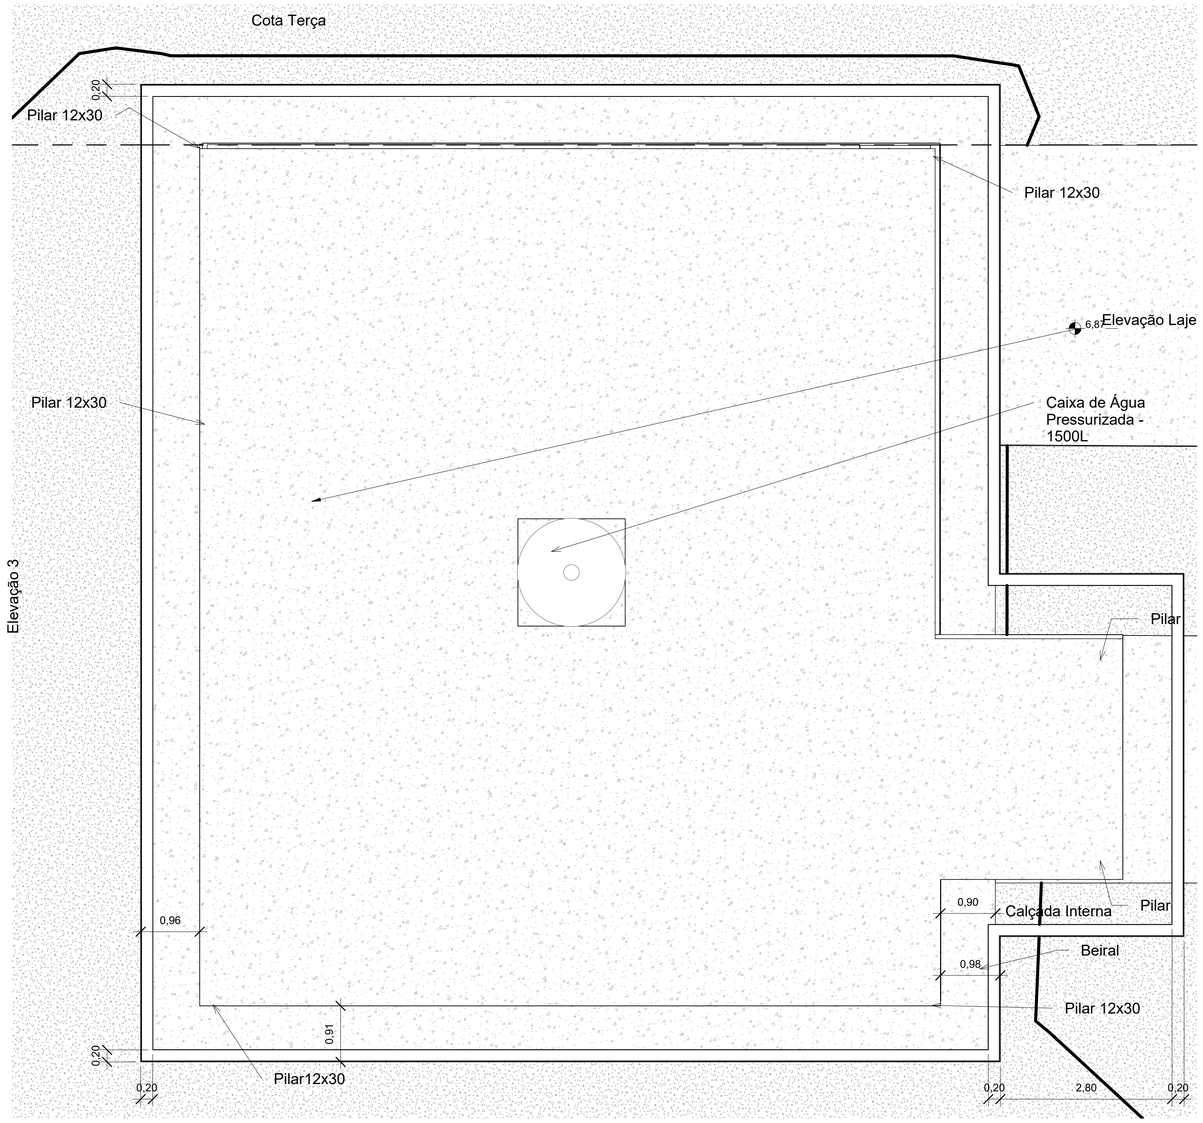

SHIS QL 23 Conjunto 3 Lote 5

PE

Projeto Executivo


Planta de Cobertura Sem Telhado

5

ALUNO: Gbriel Guimarães Horta


MAT: 222005288

ESC: 1 : 50

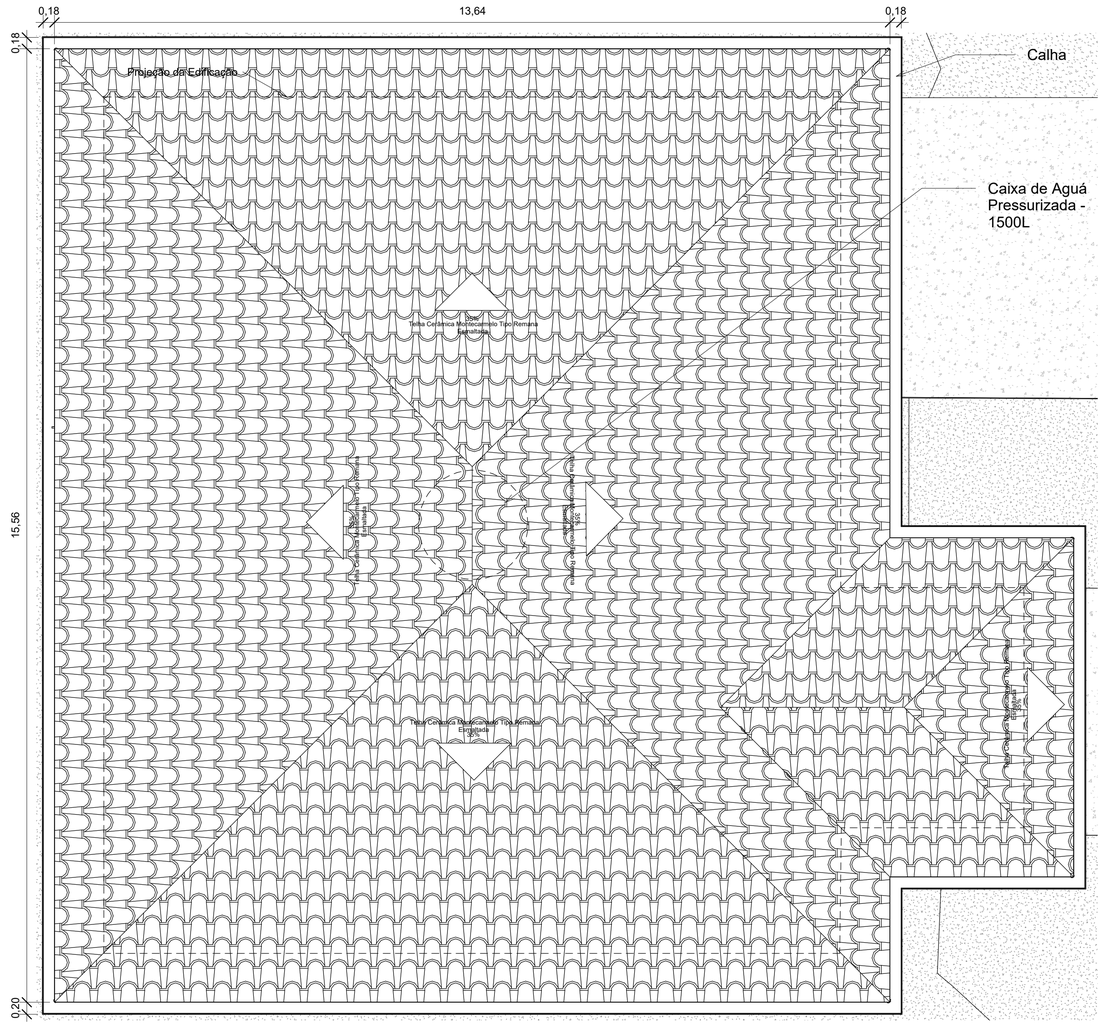


1 Planta de Cobertura
1 : 50

SHIS QL 23 Conjunto 3 Lote 5		
PE	Projeto Executivo Planta de Cobertura C. Telha	6
ALUNO: Gabriel Guimarães Horta	MAT. 222005288	ESC. 1 : 50

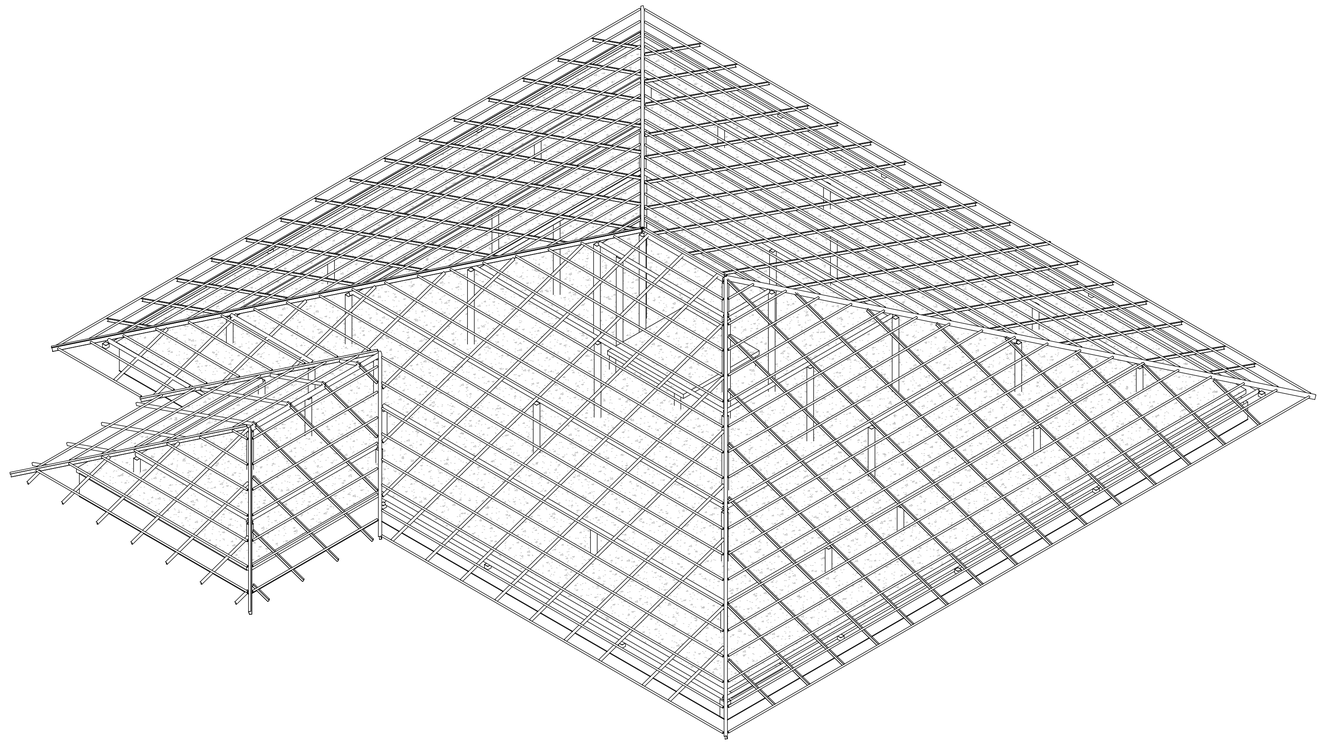


1 Estrutura Telhado 01

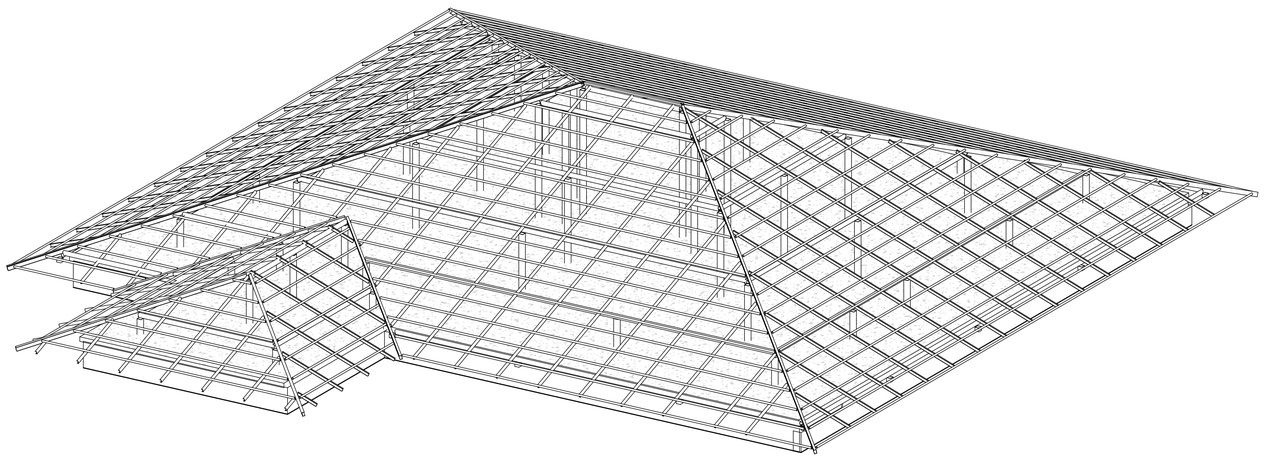


2 Estrutura Telhado 02

SHIS QL 23 Conjunto 3 Lote 5

PE	Projeto Executivo Vista Isométrica da Estrutura do Telhado	7
ALUNO: Projetista	MAT: 222005288	ESC:

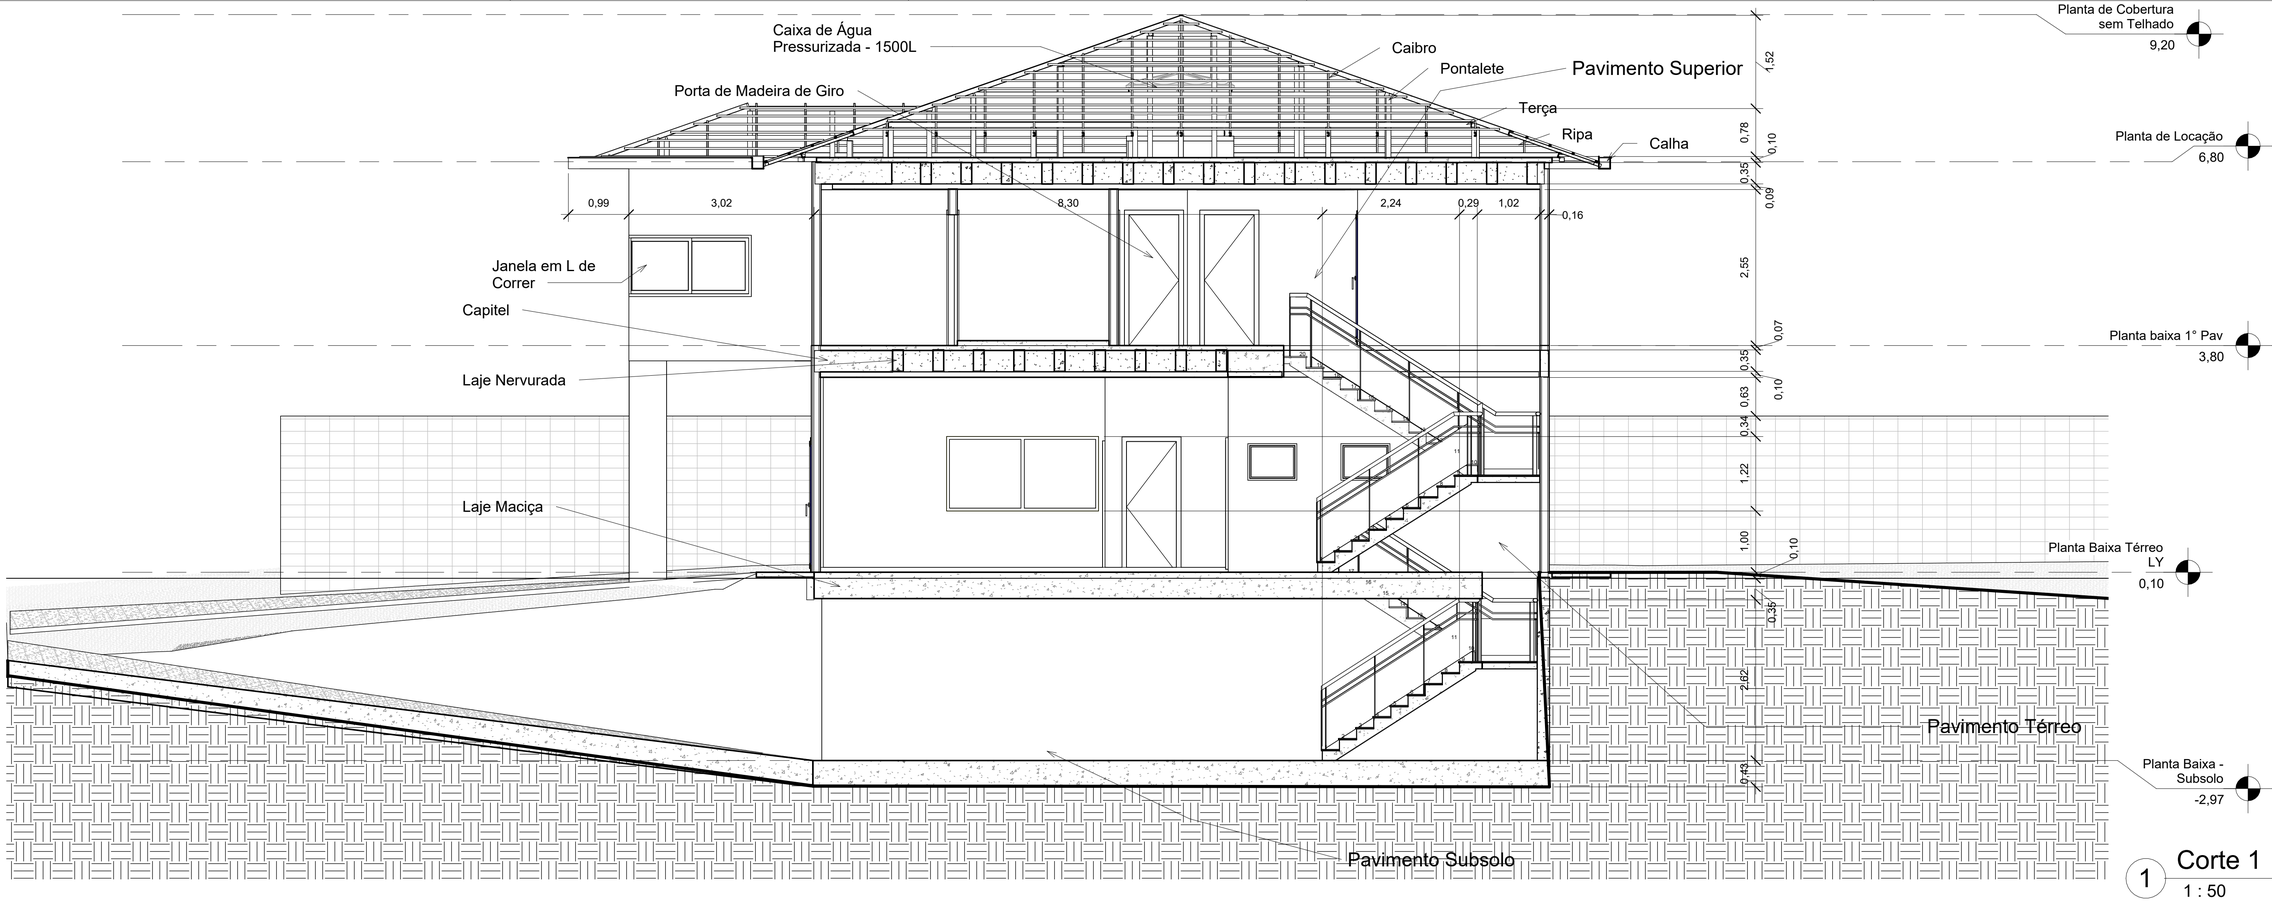


1 Corte 1
1 : 50

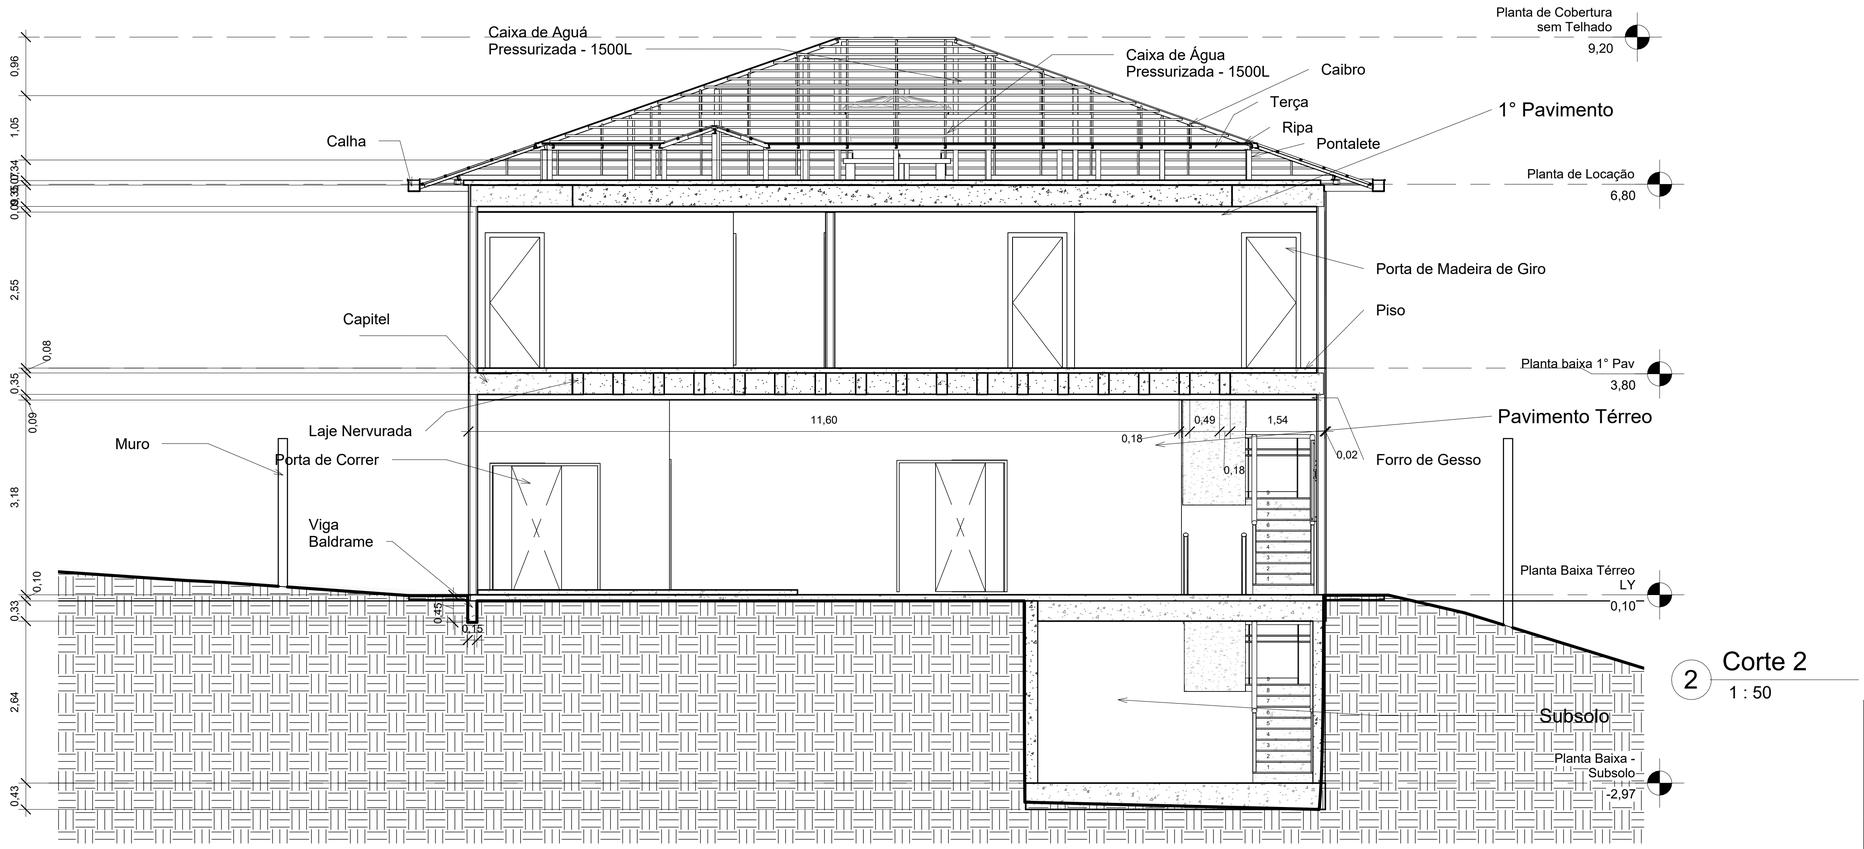

2 Corte 2
1 : 50

SHIS QL 23 Conjunto 3 Lote 5		
PE	Projeto Executivo Cortes	8
ALUNO: Gabriel Guimarães Horta	MAT.: 222005288	ESC.: 1 : 50

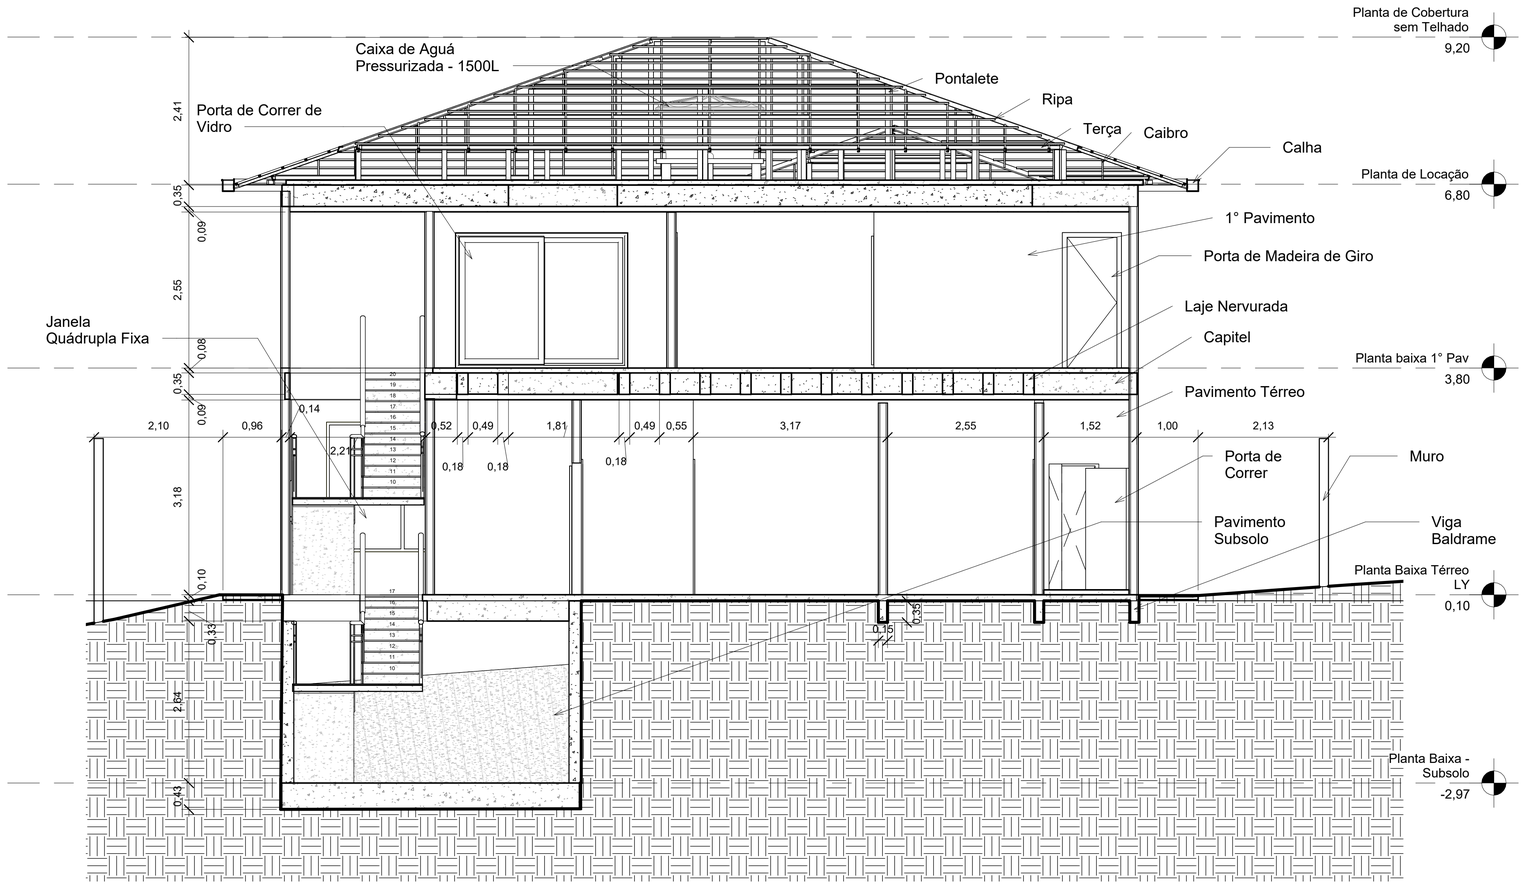


1 Corte 3
1 : 50

SHIS QL 23 Conjunto 3 Lote 5		
PE	Projeto Executivo Corte	9
ALUNO: Gabriel Guimarães Horta	MAT: 222005288	ESC: 1 : 50



1 Fachada 1


1 : 50

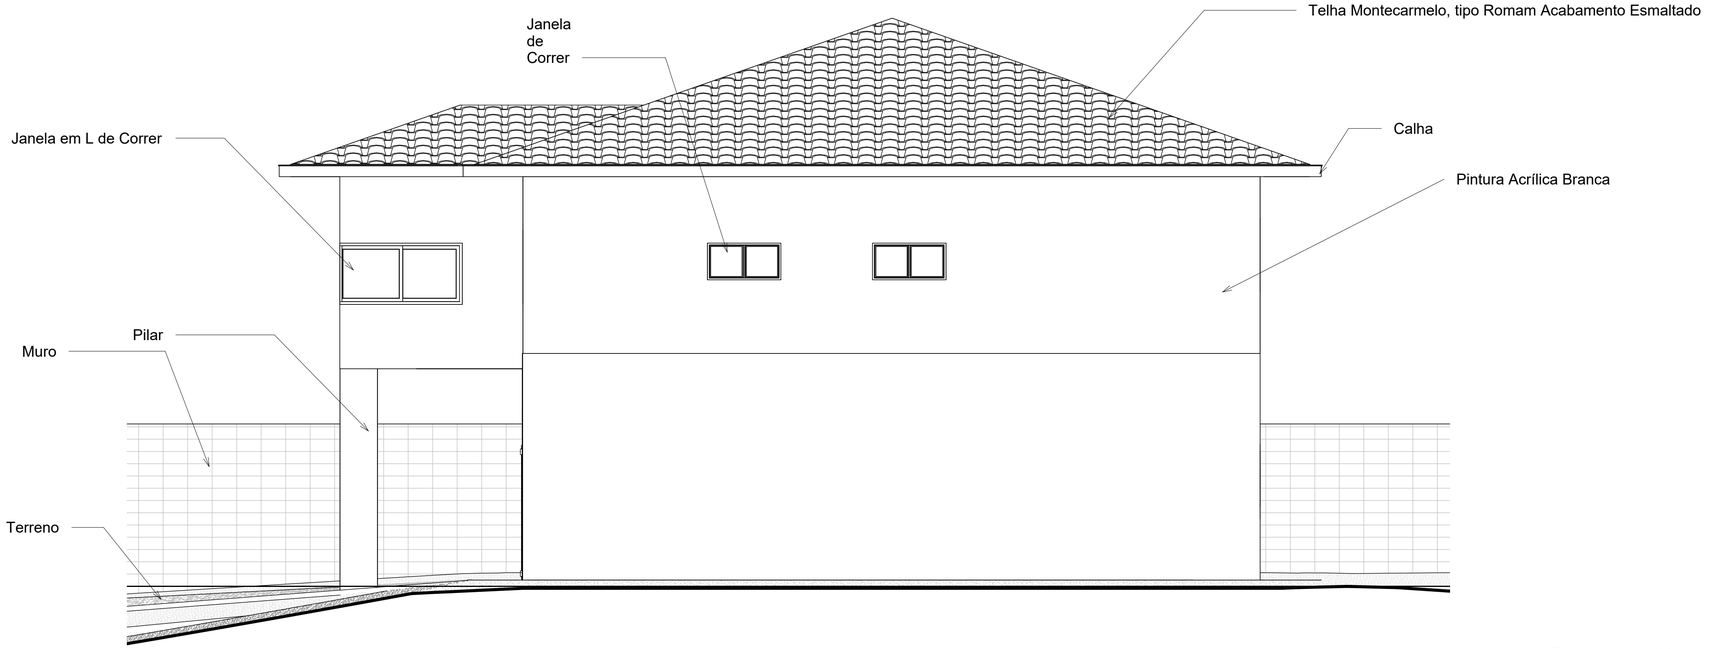

2 Fachada 2

1 : 50

SHIS QL 23 Conjunto 3 Lote 5		
PE	Projeto Executivo Vista de Fachada	10
ALUNO: Gabriel Guimarães Horta	MAT.: 222005288	ESC.: 1 : 50

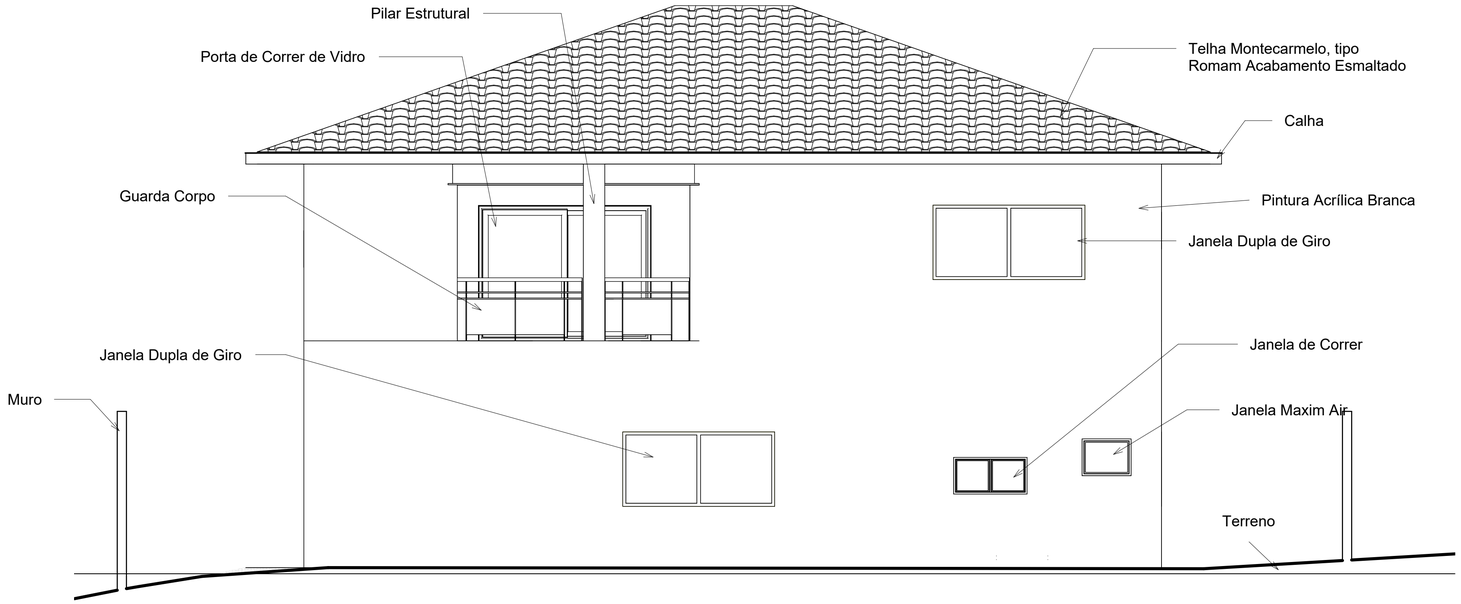

1 Fachada 3

1 : 50

SHIS QL 23 Conjunto 3 Lote 5		
PE	Projeto Executivo Vista de Fachada	11
ALUNO: Gabriel Guimarães Horta	MAT: 222005288	ESC: 1 : 50